



Zyra kadastrale / Opštinska kadastrska kancelarija: Ferizaj
 Zona kadastrale / Katastarska zona: Greme

Lloji i njësisë kadastrale / Vrsta katastarske jedinice : Parcel


Republika e Kosovës

Qeveria - Vlora-Government

Ministria e Mjedisit dhe Planifikimit Hapësiror /Ministry of Environment and Spatial Planning

AGJENCIJA KADASTRALE E KOSOVËS / KATASTARSKA AGENCJA KOSOVA/CADASTRAL AGENCY

Nr. i njësisë kadastrale / Br. katastarske jedinice : 02096-4
 32/1172-140/26
 Numri i lëndës / Broj predmeta: 042/2026
 Shkalla e zvoglimit / Razmera plana : 1:250

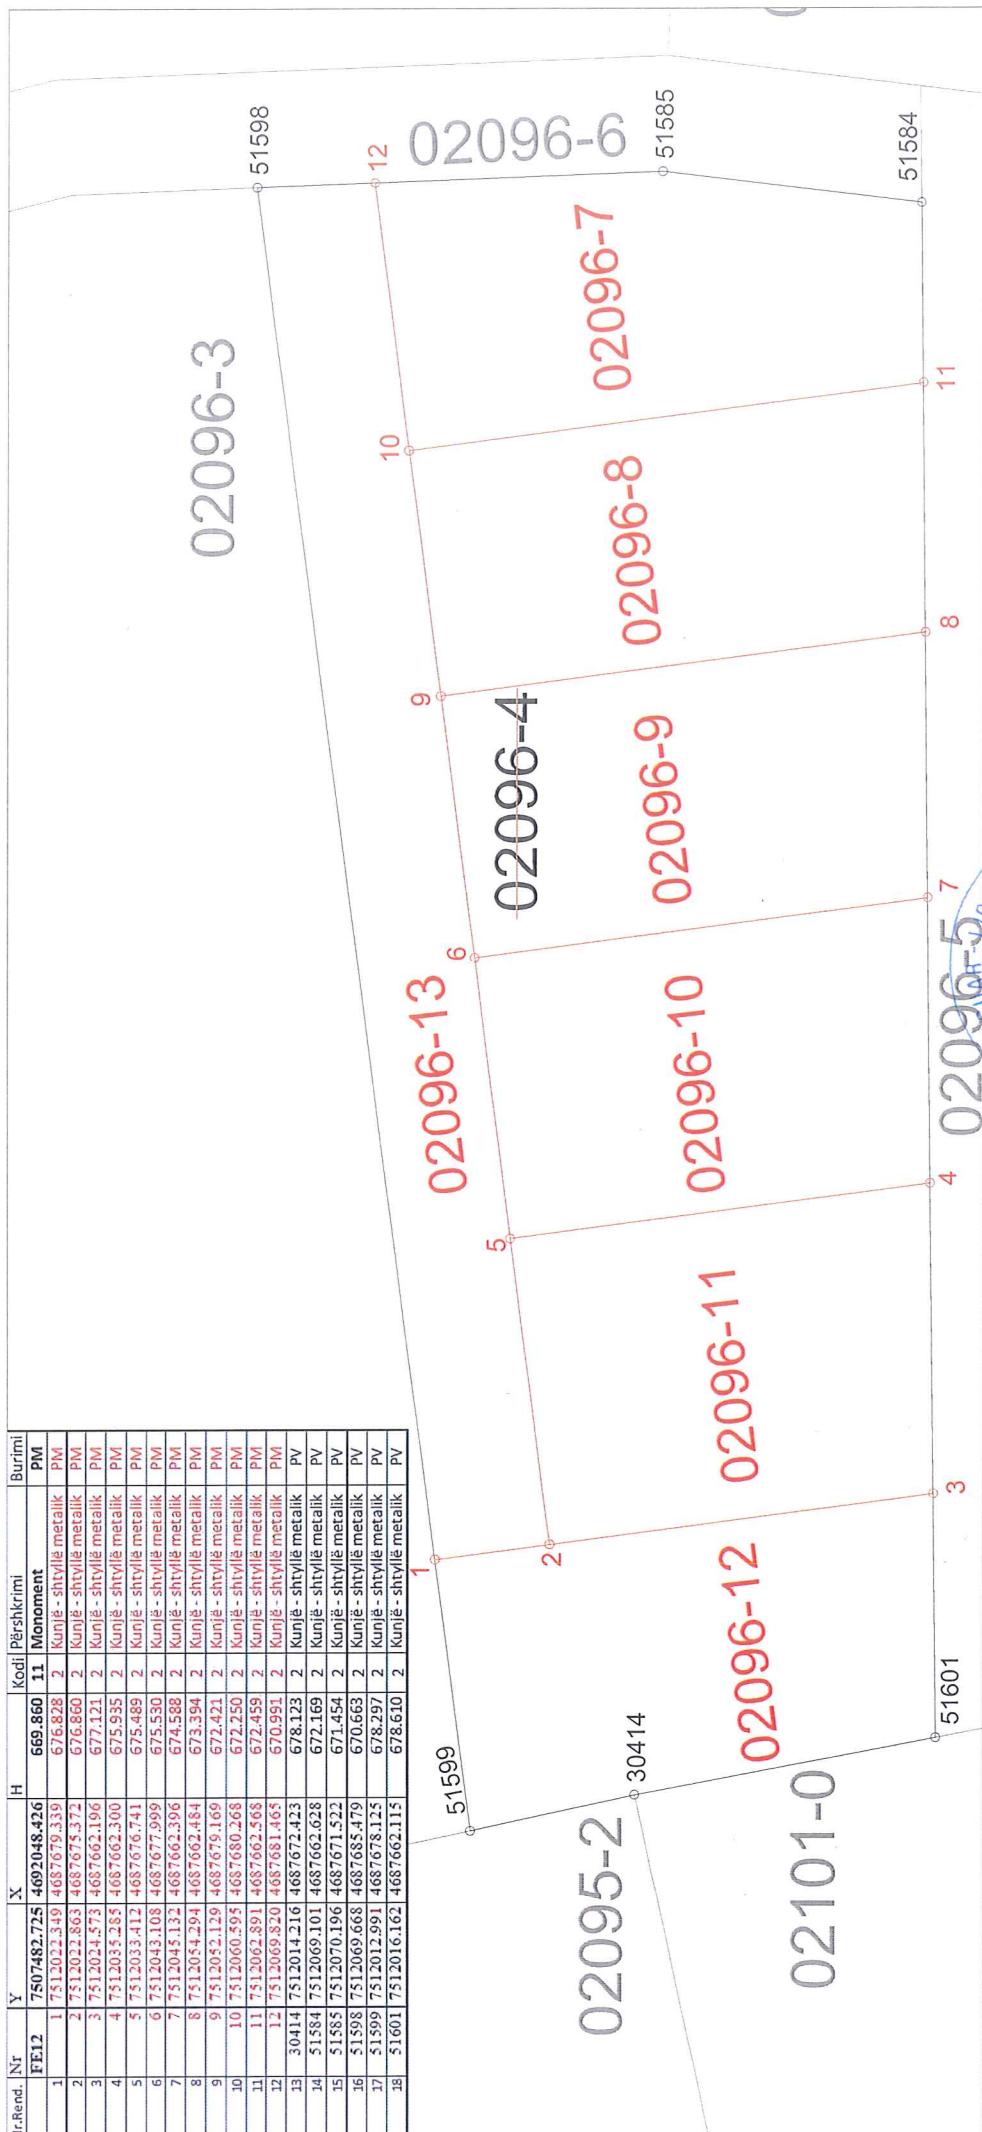

Rileyoi / Shmijo: _____
 (emri dhe mbiemri i gjecutet/kompanise/ime i prezime geodeta/ kompanije)

Nr. i licencës / Br. licence: _____
 Nënsikrimi / Potpis: _____
 Data e rilevimit / Datum shtymjanja: 21.02.2026

LURDON SEJDIU

Aprovoi / Usvojo: _____
 (emri dhe mbiemri i pësonit zyrtar/ ime i prezime sluzbeneg licit)
 Nënsikrimi / Potpis:



Aprovoi / Usvojo: _____
 (emri dhe mbiemri i pësonit zyrtar/ ime i prezime sluzbeneg licit)

Nënsikrimi / Potpis:
 Data e aprovimit / Datum usvajanja: _____